


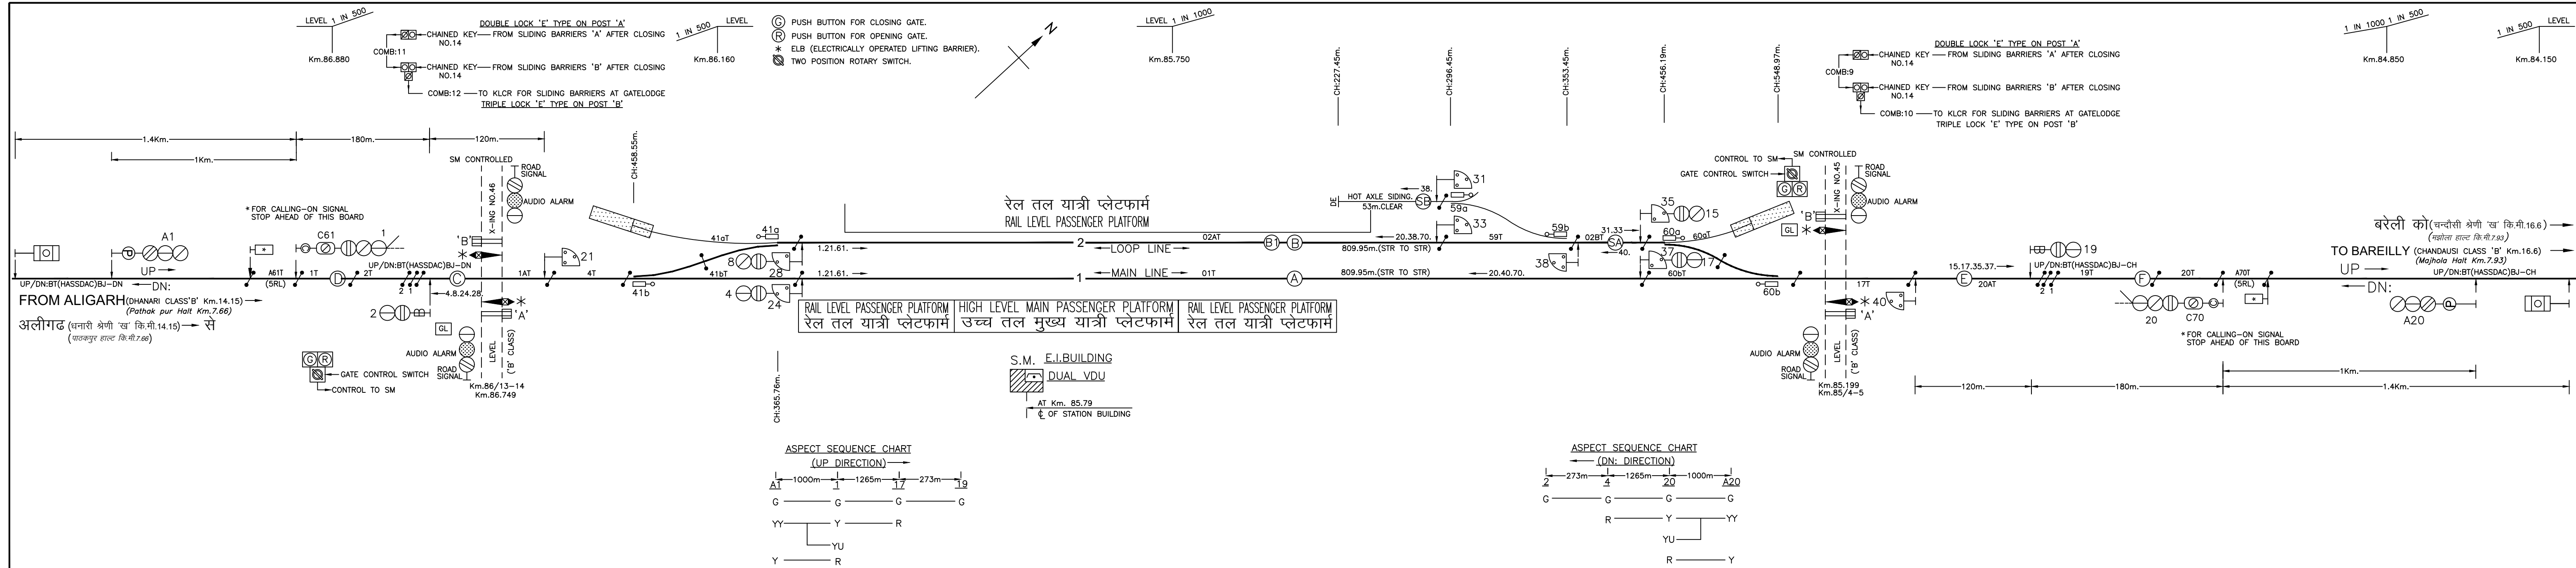

- SIGNAL SPECIFIC NOTES**
- THIS PLAN IS BASED ON THE APPROVED ESP NO.NRHOE PLAN NO.MB-18-09-2023 DATED:-25.09.2023.
 - SIGNALING INSTALLATION IS SUITABLE FOR 25KV AC TRACTION.
 - TYPE OF INTERLOCKING: CENTRALISED ELECTRONIC INTERLOCKING ALONGWITH DUAL VDU(1+1Sby) FOR THE OPERATION HAS BEEN PROVIDED.
 - BLOCK WORKING:

S.NO.	BLOCK SECTION	BLOCK WORKING
1.	BAHJOI-DHANARI	SINGLE LINE BLOCK PANEL USING UFSBI ALONGWITH HASSDAC
2.	BAHJOI-CHANDAUSSI	SINGLE LINE BLOCK PANEL USING UFSBI ALONGWITH HASSDAC

- LC GATES IN STATION SECTION:-
ALL LC GATES AS SHOWN IN THE PLAN IN THE STATION SECTION ARE INTERLOCKED AND TELEPHONICALLY CONNECTED WITH THE SM.
INTERLOCKED EMERGENCY KEYS (WITH CHAINED CRANK HANDLE FOR ELB) ARE KEPT LOCKED IN A SEALED GLAZED COVER BOX IN CUSTODY OF THE SM FOR EMERGENCY OPERATION OF THE LC GATES:-
(A) LC NO.45 'B' CLASS AT Km.85.199(85/4-5).
(B) LC NO.46 'B' CLASS AT Km.86.749(86/13-14).
- FOLLOWING NON-INTERLOCKED LC GATES IN THE BLOCK SECTION ARE TELEPHONICALLY CONNECTED WITH THE SM:-
(A) LC NO.41 'C' CLASS (CH-BJ) AT Km.79/1-78/15.
(B) LC NO.42 'C' CLASS (CH-BJ) AT Km.81/1-80/12.
(C) LC NO.49 'C' CLASS (DN-BJ) AT Km.83/6-7(83.379).
- TRACK CIRCUITING:-MSDAC HAS BEEN PROVIDED IN THE ENTIRE YARD.
- THE FM OF CONVERGING X-OVER IN A LINE SHALL BE CONSIDERED AS THE SJ OF THE X-OVER POINT IN THE ADJACENT LINE.
- NUMBERING OF SIGNALS & POINTS:-

FUNCTIONS	DIRECTION	RANGE	SPARES
SIGNAL	UP	S-1 TO S-19 (ODD NUMBERS)	3.5.7.9.11.13.
	DN	S-2 TO S-20 (EVEN NUMBERS)	6.10.12.14.16.18.
SHUNT SIGNAL	UP	SH-21 TO SH-39 (ODD NUMBERS)	23.25.27.29.39.
	DN	SH-22 TO SH-40 (EVEN NUMBERS)	22.26.30.32.34.36.
POINTS	-	41-60	42.43.44.45.46.47.48.49.50. 51.52.53.54.55.56.57.58.
	-	61-69 (ODD NUMBERS)	63.65.67.69.
Co-ON	UP	61-69 (ODD NUMBERS)	63.65.67.69.
	DN	62-70 (EVEN NUMBERS)	62.64.66.68.

- POINT CRANK HANDLES:-
THE CRANK HANDLE FOR EACH GROUP SHALL HAVE DIFFERENT WARD WITH POINT MACHINES HAVING MATCHING SPIGOTS.
THE FOLLOWING CRANK HANDLE GROUPS ARE PROVIDED :-
- | GROUP | POINTS |
|-------|--------|
| CHO1 | 41a/b |
| CHO2 | 59a/b |
| CHO3 | 60a/b |
- ALL CRANK HANDLES ARE KEPT IN THE LOCATION BOX ONLY.

11. DESCRIPTIONS OF ROUTES AND OVERLAPS:-

S.NO.	SIGNAL NO.	ROUTE	OVERLAP POINTS(N/R)	TC UPTO
1.	1	A	60N	20aT
2.	1	B	60N	60aT
3.	1	B1	60R	20aT
4.	20	A	41N	1aT
5.	20	B	41N	41aT
6.	20	B1	41R	1aT

12. ISOLATION:-

FOLLOWING ISOLATION HAS BEEN PROVIDED FOR MAIN/CO-ON SIGNALS ROUTE IN TERMS OF GR PARA 5.16 AND OTHER PERMISSIONS.

S.NO.	MAIN/CO-ON ROUTE	POINTS LOCKED (N/R)	MAIN SIGNAL/C-ON ROUTES LOCKED	SHUNT SIGNALS ROUTES LOCKED
1.	S1-A	NIL	NIL	NIL
2.	S1-B/C61-B	NIL	70A	40A
3.	S1-B1	NIL	NIL	NIL
4.	S20-A	NIL	NIL	NIL
5.	S20-B/C70-B	NIL	61A	21A
6.	S20-B1	NIL	NIL	NIL
7.	S4-C	NIL	NIL	NIL
8.	B-C	NIL	70A	40A
9.	15-E	NIL	61A	21A
10.	S17-E	NIL	NIL	NIL
11.	C61-A	NIL	15E.20B.70B	35E.40B
12.	C70-A	NIL	8C.1B.61B	28C.21B

- THE 'OFF' ASPECT OF A STARTER SIGNAL SHALL BE RELEASED BY THE 'OFF' ASPECT OF THE ADVANCED STARTER SIGNAL.
- SPECIAL FEATURES:-
(A). ALL LOOP LINE STARTER SIGNALS ARE APPROACH CLEARED.

NO. OF ROUTES:-24
FIELD UNIT: DY.CSTE/GSU/MB
UPGRADATION OF INTERLOCKING FROM STD.I TO STD.II
WITH ELECTRONIC INTERLOCKING

ROK...03.10.2023
ROK...11.10.2023
ROK...12.10.2023
ROK...AS...18.10.2023
ROK...JK...21.10.2023
RA...JK...03.11.2023
ROK...AVN...29.11.2023

-54-

07.11.23

DY.CSTE/GSU/MB

AKSHAI KUMAR

Digitally signed by AKSHAI KUMAR
DN: cn=AKSHAI KUMAR, o=SR.DSTE/MB, email=akshai.kumar@rrcc.co.in, c=IN

SR.DSTE/MB

ASHISH SINGH

Digitally signed by ASHISH SINGH
DN: cn=ASHISH SINGH, o=SR.DOM/MB, email=ashish.singh@rrcc.co.in, c=IN

SR.DOM/MB

उत्तर प्रदेश
मुरादाबाद
(MB)

(ROBINS KUMAR)

अनुमोदित
वर्तमान प्रमाणित
CAO BY JET/DMD

JITENDRA KUMAR GANDEWAR

Digitally signed by JITENDRA KUMAR GANDEWAR
DN: cn=JITENDRA KUMAR GANDEWAR, o=SR.DSTE/MB, email=jitendra.kumar@rrcc.co.in, c=IN

SR.DSTE/MB

VIKAS MAHOLA

Digitally signed by VIKAS MAHOLA
DN: cn=VIKAS MAHOLA, o=SR.DSTE/MB, email=vikas.mahola@rrcc.co.in, c=IN

SR.DSTE/MB

RIKHA KULKARNI

Digitally signed by RIKHA KULKARNI
DN: cn=RIKHA KULKARNI, o=SR.DSTE/MB, email=riika.kulkarni@rrcc.co.in, c=IN

SR.DSTE/MB

RAJ KUMAR SINGH

Digitally signed by RAJ KUMAR SINGH
DN: cn=RAJ KUMAR SINGH, o=SR.DSTE/MB, email=raj.kumar@rrcc.co.in, c=IN

SR.DSTE/MB

NIRAJ SAHAY

Digitally signed by NIRAJ SAHAY
DN: cn=NIRAJ SAHAY, o=SR.DSTE/MB, email=niraj.sahay@rrcc.co.in, c=IN

SR.DSTE/MB

VIJAY KUMAR PANDEY

Digitally signed by VIJAY KUMAR PANDEY
DN: cn=VIJAY KUMAR PANDEY, o=SR.DSTE/MB, email=vijay.kumar@rrcc.co.in, c=IN

SR.DSTE/MB

संकेत एवं अन्तर्भाषीन विन्यास
SIGNAL & INTERLOCKING PLAN
(ELECTRONIC INTERLOCKING) (STD.-II)

COMP: ON

बहजोई
BAHJOI (BJ)
(श्रेणी 'ख')

SUPERSEDES I/P NO.

NO.S-IP
7543

BAHJOI-IP-MB-NR

Status: freigegeben

DCC: EFS OKZ Leistung: TEC

Intern

Siemens M0; Dokument-ID: PM2 A6Z00057352367 000 A